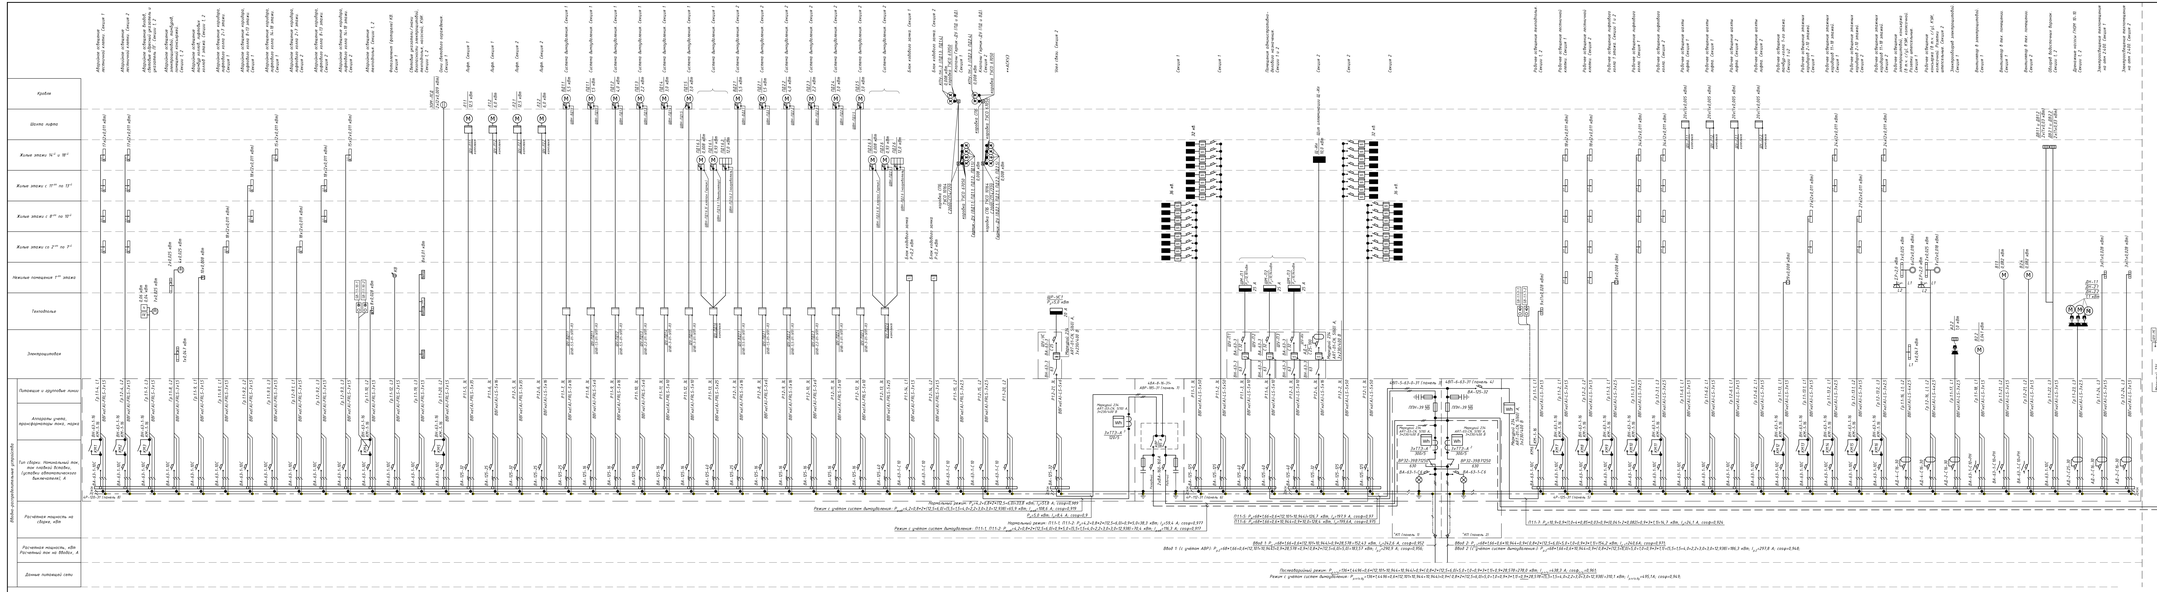
Крыши
Шахта лифта
Кладка этажа N-2 и N-1
Кладка этажа с 11-го по 15-й
Кладка этажа с 8-го по 10-й
Кладка этажа со 2-го по 7-й
Нижняя отметка 1-го этажа
Техподполье
Электрощитовая
Питающие и групповые линии
Аппараты учета, преобразователи тока, напряжения
Тип сборки (Номинальный ток или уставка блокиров., Трубопроводы обвинчиваемые бронированные), А
Расчетная мощность на сборке, кВт
Расчетный ток на Вводе, А
Данные питающей сети
Вводы распределительные устройства
ГРУ1.1-2 ВВГнг(А)-LS-0,66 4х185 ПВ4 ПВ3 ПВ2 ПВ1 ВА-99-1 ВА-99-1 ВА-99-